





WHZ Westsächsische
Hochschule Zwickau
University of Applied Sciences



IEV Institut für Energie und Verkehr
Department of Energy and Transport Engineering

PO box 201037
D-08012 Zwickau

Tel.: +49 (0) 375 536 3443
Fax: +49 (0) 375 536 3393

Email: iev@fh-zwickau.de
URL: www.fh-zwickau.de/iev

Course: Urban Traffic Facilities Design Project
Under Guidance of: Prof. Felix Rudolph
Mr. Michael Müller
Mr. Dennis Saputra

Date : 05th June 2025

Technical Drawing of Carl von Ossietzky Straße, Chemnitz

S.No	Description	Value
1	Section	1
2	Section starting from	Claus Straße
3	Section ending at	Heimgarten
4	Section length	244m
5	Section width	20m

SHEET NO: 1

Drawn by Group 3 (Road Traffic Engineering)

Names of the Group members
Abdul Hadi Mohammed
Rahil Asit Maviya
Fatemeh Heidari
Abdul Samad
Dikshant Patel
Akhil Jacob Kolathu

Scale (1:500)

ALL THE MEASUREMENTS ARE IN METERS





WHZ Westsächsische
Hochschule Zwickau
University of Applied Sciences



Institut für Energie und Verkehr
Department of Energy and Transport Engineering

PO box 201037 Tel.: +49 (0) 375 536 3443 Email: iev@fh-zwickau.de
D-08012 Zwickau Fax: +49 (0) 375 536 3393 URL: www.fh-zwickau.de/iev

Course: Urban Traffic Facilities Design Project Date : 05th June 2025
Under Guidance of: Prof. Felix Rudolph
Mr. Michael Müller
Mr. Dennis Saputra

Technical Drawing of Carl von Ossietzky Straße, Chemnitz

S.No	Description	Value
1	Section	2.2
2	Section starting from	Heimgarten
3	Section ending at	Geibel Straße
4	Section length	716m
5	Section width	23.7m

SHEET NO: 3

Drawn by Group 3 (Road Traffic Engineering)

Names of the Group members

Abdul Hadi Mohammed
Rahil Asit Maviya
Fatemeh Heidari
Abdul Samad
Dikshant Patel
Akhil Jacob Kolathu

Scale (1:500)



ALL THE MEASUREMENTS ARE IN METERS





WHZ Westsächsische
Hochschule Zwickau
University of Applied Sciences



Institut für Energie und Verkehr
Department of Energy and Transport Engineering

PO box 201037 Tel.: +49 (0) 375 536 3443 Email: iev@fh-zwickau.de
D-08012 Zwickau Fax: +49 (0) 375 536 3393 URL: www.fh-zwickau.de/iev

Course: Urban Traffic Facilities Design Project Date : 05th June 2025
Under Guidance of: Prof. Felix Rudolph
Mr. Michael Müller
Mr. Dennis Saputra

Technical Drawing of Carl von Ossietzky Straße, Chemnitz

S.No	Description	Value
1	Section	2.3
2	Section starting from	Heimgarten
3	Section ending at	Geibel Straße
4	Section length	716m
5	Section width	23.7m

SHEET NO: 4

Drawn by Group 3 (Road Traffic Engineering)

Names of the Group members

Abdul Hadi Mohammed
Rahil Asit Maviya
Fatemeh Heidari
Abdul Samad
Dikshant Patel
Akhil Jacob Kolathu

Scale (1:500)



ALL THE MEASUREMENTS ARE IN METERS





WHZ Westsächsische
Hochschule Zwickau
University of Applied Sciences



IEV Institut für Energie und Verkehr
Department of Energy and Transport Engineering

PO box 201037
D-08012 Zwickau

Tel.: +49 (0) 375 536 3443
Fax: +49 (0) 375 536 3393

Email: iev@fh-zwickau.de
URL: www.fh-zwickau.de/iev

Course: Urban Traffic Facilities Design Project
Under Guidance of: Prof. Felix Rudolph
Mr. Michael Müller
Mr. Dennis Saputra

Date : 05th June 2025

Technical Drawing of Carl von Ossietzky Straße, Chemnitz

S.No	Description	Value
1	Section	3
2	Section starting from	Geibel Straße
3	Section ending at	Hans Zeigler Straße
4	Section length	261m
5	Section width	16.6m to 18m

SHEET NO: 5

Drawn by Group 3 (Road Traffic Engineering)

Names of the Group members

Abdul Hadi Mohammed
Rahil Asit Maviya
Fatemeh Heidari
Abdul Samad
Dikshant Patel
Akhil Jacob Kolathu

Scale (1:500)



ALL THE MEASUREMENTS ARE IN METERS





WHZ Westsächsische
Hochschule Zwickau
University of Applied Sciences



IEV Institut für Energie und Verkehr
Department of Energy and Transport Engineering

PO box 201037
D-08012 Zwickau

Tel.: +49 (0) 375 536 3443
Fax: +49 (0) 375 536 3393

Email: iev@fh-zwickau.de
URL: www.fh-zwickau.de/iev

Course: Urban Traffic Facilities Design Project
Under Guidance of: Prof. Felix Rudolph
Mr. Michael Müller
Mr. Dennis Saputra

Date : 05th June 2025

Technical Drawing of Carl von Osseitzky Straße, Chemnitz

S.No	Description	Value
1	Section	4
2	Section starting from	Hans Zeigler Straße
3	Section ending at	Carl-Von-Osseitzky Straße
4	Section length	264m
5	Section width	13.3m

SHEET NO: 6

Drawn by Group 3 (Road Traffic Engineering)


Names of the Group members

Abdul Hadi Mohammed
Rahil Asit Maviya
Fatemeh Heidari
Abdul Samad
Dikshant Patel
Akhil Jacob Kolathu

Scale (1:500)



ALL THE MEASUREMENTS ARE IN METERS

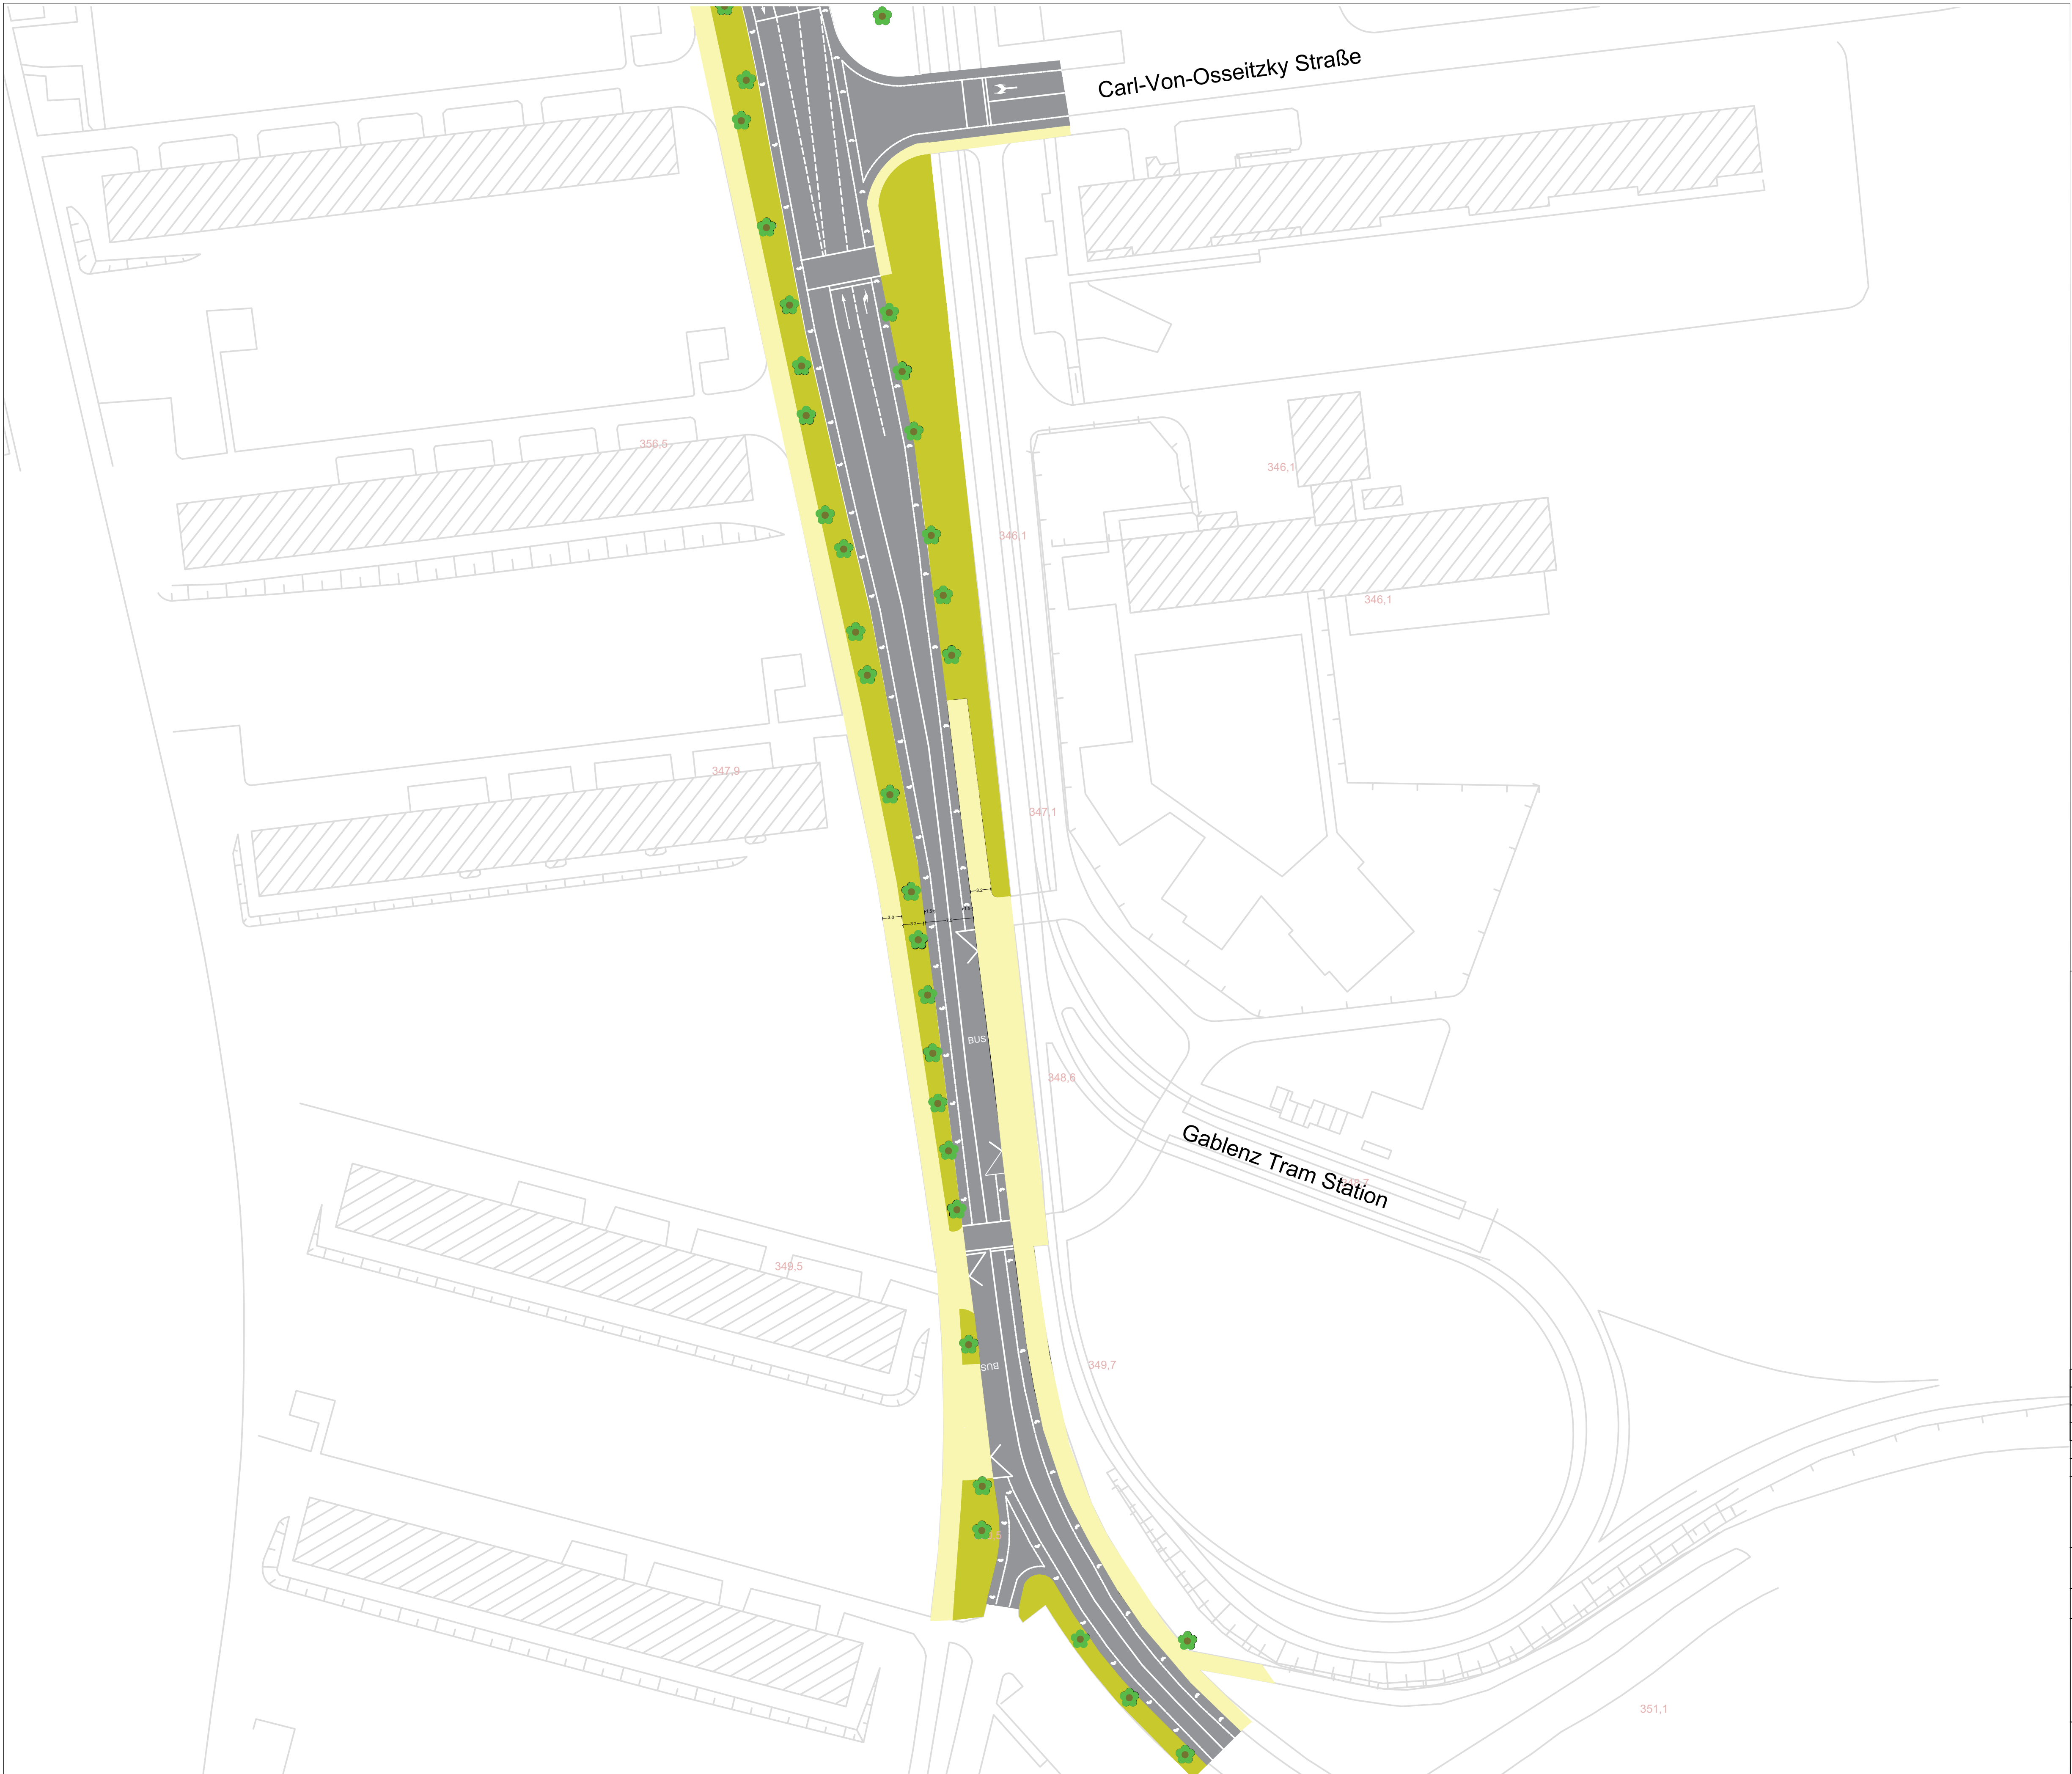



WHZ Westsächsische
Hochschule Zwickau
University of Applied Sciences



IEV Institut für Energie und Verkehr
Department of Energy and Transport Engineering

PO box 201037
D-08012 Zwickau

Tel.: +49 (0) 375 536 3443
Fax: +49 (0) 375 536 3393

Email: iev@fh-zwickau.de
URL: www.fh-zwickau.de/iev

Course: Urban Traffic Facilities Design Project
Under Guidance of: Prof. Felix Rudolph
Mr. Michael Müller
Mr. Dennis Saputra

Date : 05th June 2025

Technical Drawing of Carl von Osseitzky Straße, Chemnitz

S.No	Description	Value
1	Section	5
2	Section starting from	Carl-Von-Osseitzky Straße
3	Section ending at	Gablenz Tram Station
4	Section length	292m
5	Section width	16.7m (Varies)

SHEET NO: 7

Drawn by Group 3 (Road Traffic Engineering)

Names of the Group members

Abdul Hadi Mohammed
Rahil Asit Maviya
Fatemeh Heidari
Abdul Samad
Dikshant Patel
Akhil Jacob Kolathu

Scale (1:500)



ALL THE MEASUREMENTS ARE IN METERS